
REFERENCE	PLANT DISTRIBUTION BOARD				
COMPARTMENT					
TYPE/ SIZE					
WB REF					
DESCRIPTION	GANTRY CRANE SUPPLY	STORM TRANSFER ACTUATED VALVE NO.1	STORM TRANSFER ACTUATED VALVE NO.2	EXTERNAL LIGHTING	MAINS INCOMER
TAG		KNUTF-NP1-NA1-PMS01-VA001	KNUTF-NP1-NA1-PMS01-VA002		

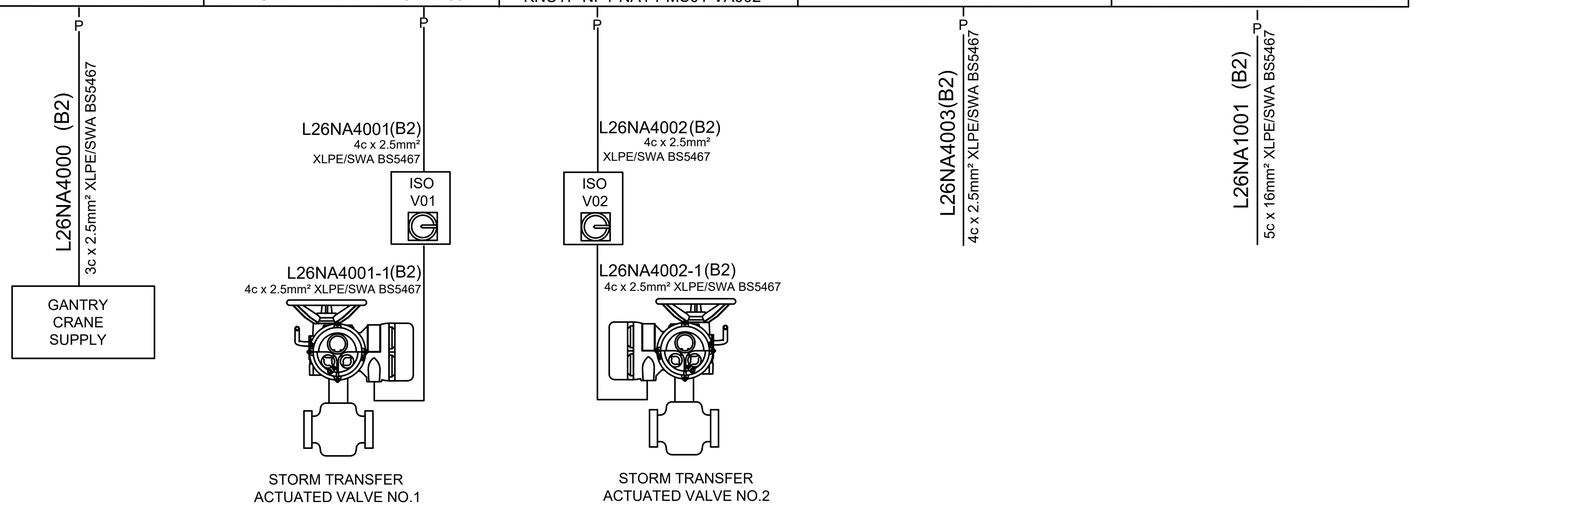

WARD & BURKE

BIM QUALITY SHEET NO:

COPYRIGHT: This drawing is protected by copyright and is not to be reproduced in part or whole form without the prior and written consent of Ward & Burke.

NOTES

REV NO:	DESCRIPTION	DATE	BY
P01	For Information	27/07/6	DG

United Utilities
Water for the North West

PROJECT:
Knutsford WwTW

TITLE:
Plant DB

DRAWN BY:	CHECKED BY:	DATE:
AS	DG	21/04/2026

SHEET SIZE:	PROJECT NUMBER:
A1	C783 - KNUTDT

W&B DRAWING No:	REV:
KNUTDT-WAB-03-XX-DR-W-60204	P01

CLIENT DRAWING No:	SCALE:
	NTS

CAD FILE: KNUTDT-WAB-03-XX-M2-W-60200-BCD

SUITABILITY CODE:
S01 - For Information