
REFERENCE	BUILDING SERVICES DISTRIBUTION BOARD							
COMPARTMENT								
TYPE/ SIZE	25A BS88	60898 - S/P - MCB / 16 AMP TYPE B	60898 - S/P - MCB / 6 AMP TYPE B	60898 - S/P - MCB / 6 AMP TYPE C	60898 - S/P - MCB / 6 AMP TYPE B	60898 - S/P - MCB / 6 AMP TYPE B	60898 - S/P - MCB / 6 AMP TYPE B	
WB REF								
DESCRIPTION	MAINS SUPPLY	SOCKET	HEATER	EXTRACTOR FAN	INTERNAL LIGHTS	FIRE ALARM	TELEMETRY OUTSTATION	
WAY		WAY 1 L1	WAY 1 L2	WAY 1 L3	WAY 2 L1	WAY 2 L3	WAY 3 L1	

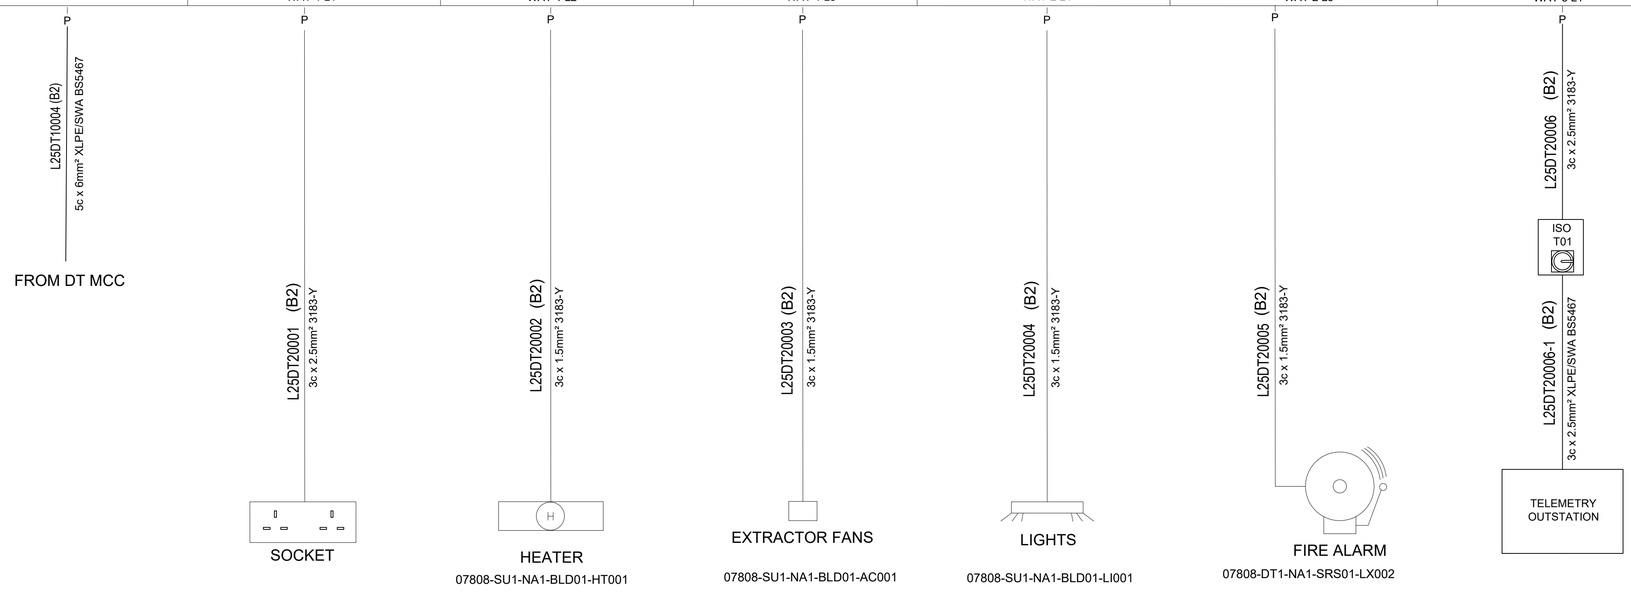

WARD & BURKE

BIM QUALITY SHEET NO:

COPYRIGHT: This drawing is protected by copyright and is not to be reproduced in part or whole form without the prior and written consent of Ward & Burke.

NOTES

1.

REV NO:	DESCRIPTION	DATE	BY
P01	For Information	18/08/25	DG

United Utilities
Water for the North West

PROJECT:

Philips Road

TITLE:

Building Services BCD

DRAWN BY:	CHECKED BY:	DATE:
DG	JF	18/08/25

SHEET SIZE:	PROJECT NUMBER:
A1	C809 - PHRDET

W&B DRAWING No:	REV:
PHRDET-WAB-01-XX-DR-W-60103	P01

CLIENT DRAWING No:	SCALE:
80065614-01-WAB-05062-NA-DR-E-00004	NTS

CAD FILE: PHRDET-WAB-01-XX-M2-W-60100-BCD

SUITABILITY CODE:
S2 - Suitable For Information