
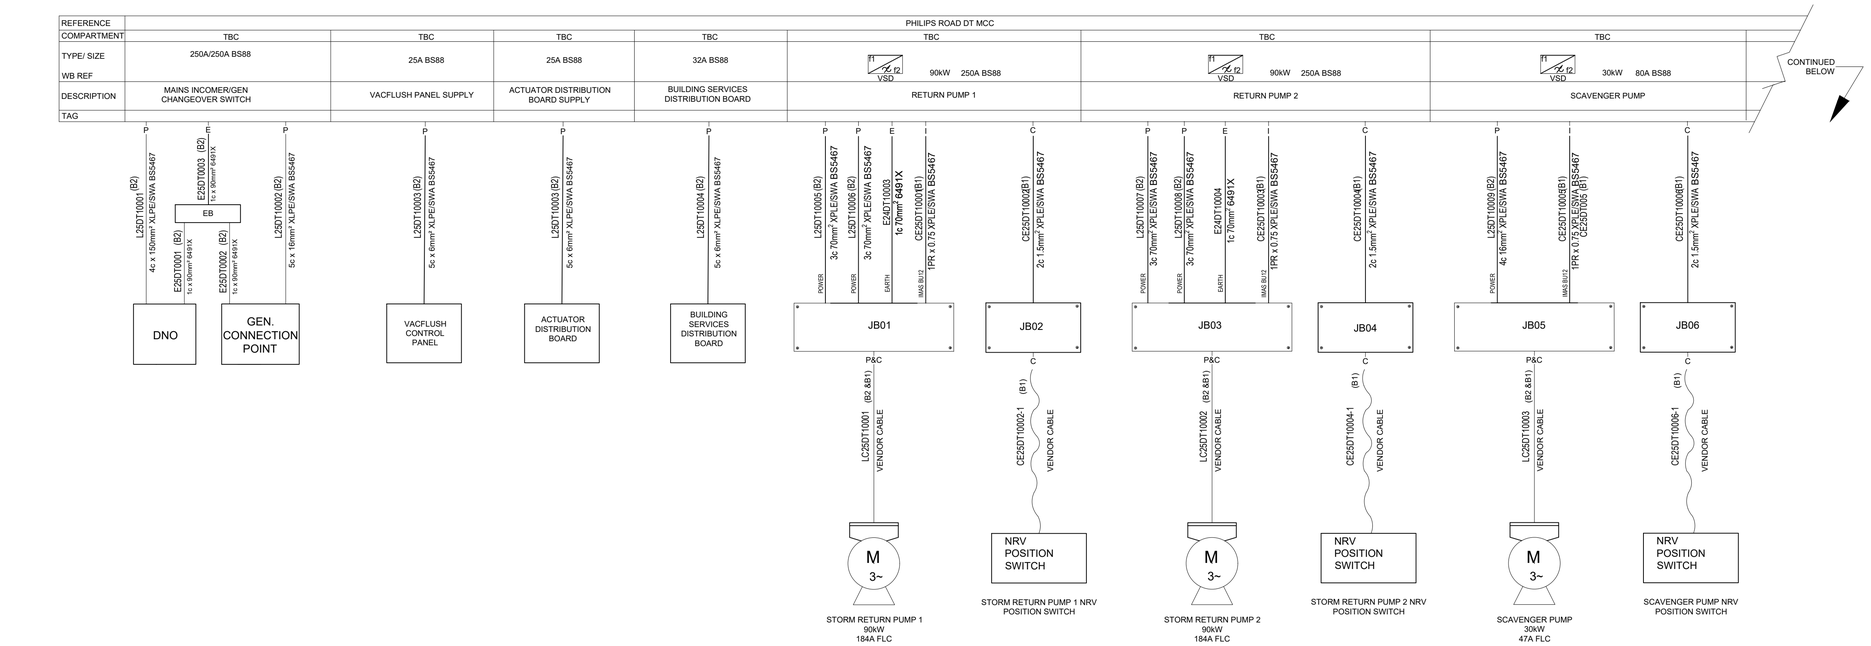


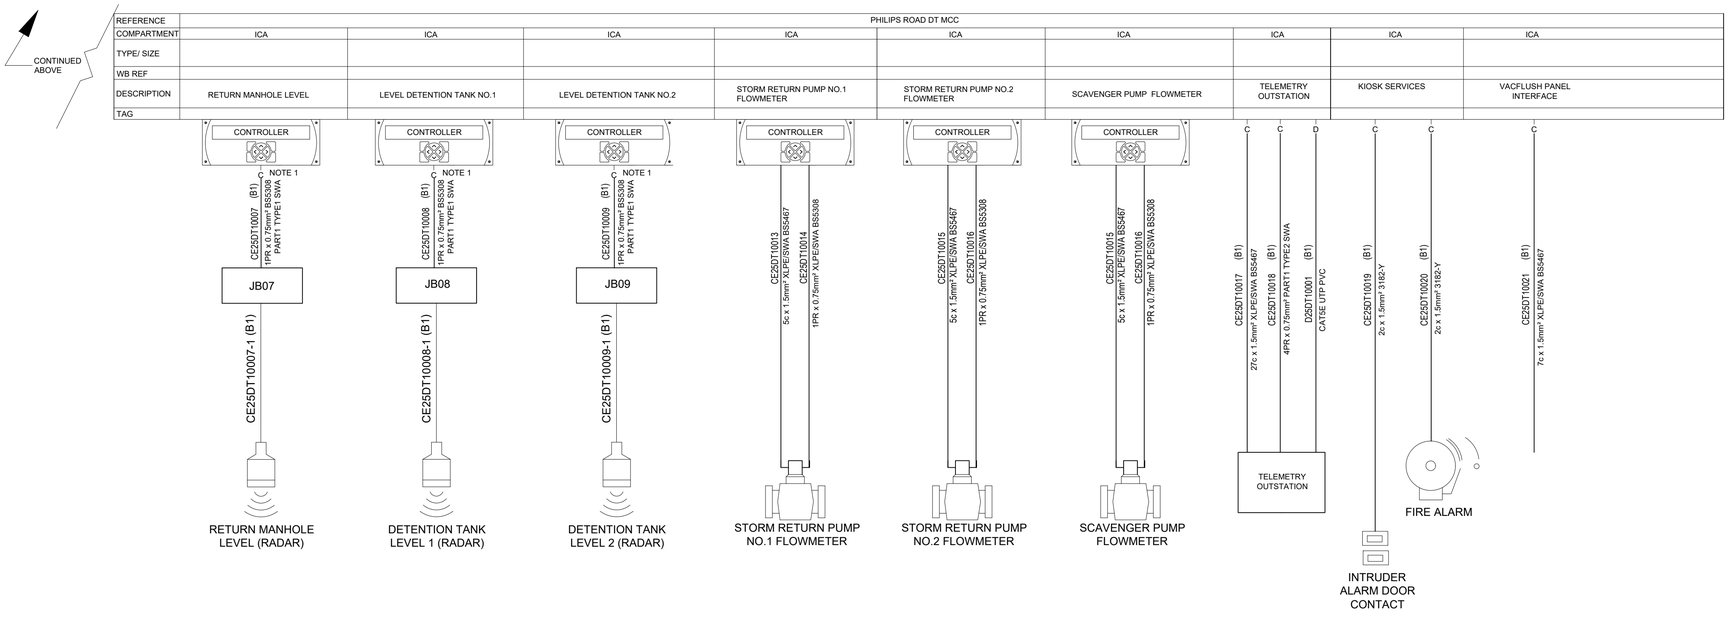

WARD & BURKE

BIM QUALITY SHEET NO:

COPYRIGHT: This drawing is protected by copyright and is not to be reproduced in part or whole form without the prior and written consent of Ward & Burke.

NOTES

REV NO:	DESCRIPTION	DATE	BY
P01	For Information	18/08/25	DG

United Utilities
Water for the North West

PROJECT:

Philips Road

TITLE:

MCC BCD

DRAWN BY:	CHECKED BY:	DATE:
DG	JF	18/08/25

SHEET SIZE:	PROJECT NUMBER:
A1	C809 - PHRDET

W&B DRAWING No: **PHRDET-WAB-01-XX-DR-W-60101** REV: P01

CLIENT DRAWING No: 80065614-01-WAB-05062-NA-DR-E-00002 SCALE: NTS

CAD FILE: PHRDET-WAB-01-XX-M2-W-60100-BCD

SUITABILITY CODE: S2 - Suitable For Information