

REFERENCE	PHILIPS ROAD VACFLUSH PANEL - Form 2a								
COMPARTMENT									
TYPE/ SIZE WB REF	25A BS88	DOL 2.2kW 6A BS88							
DESCRIPTION	MAINS SUPPLY	VACUUM PUMP (DUTY)	NEW VACFLUSH SYSTEM LEVEL SWITCH	NEW VACFLUSH SYSTEM PRESSURE SWITCH NO.1	NEW VACFLUSH SYSTEM PRESSURE SWITCH NO.2	P & V ISOLATION VALVE NO.1	P & V ISOLATION VALVE NO.2	FLUSHING (ACTUATED) VALVE NO.3	MCC - PUMPING STATION INTERFACE
TAG						XXXXX-DT1-NA1-STO01-VA001	XXXXX-DT1-NA1-STO01-VA002	XXXXX-DT1-NA1-STO01-VA003	

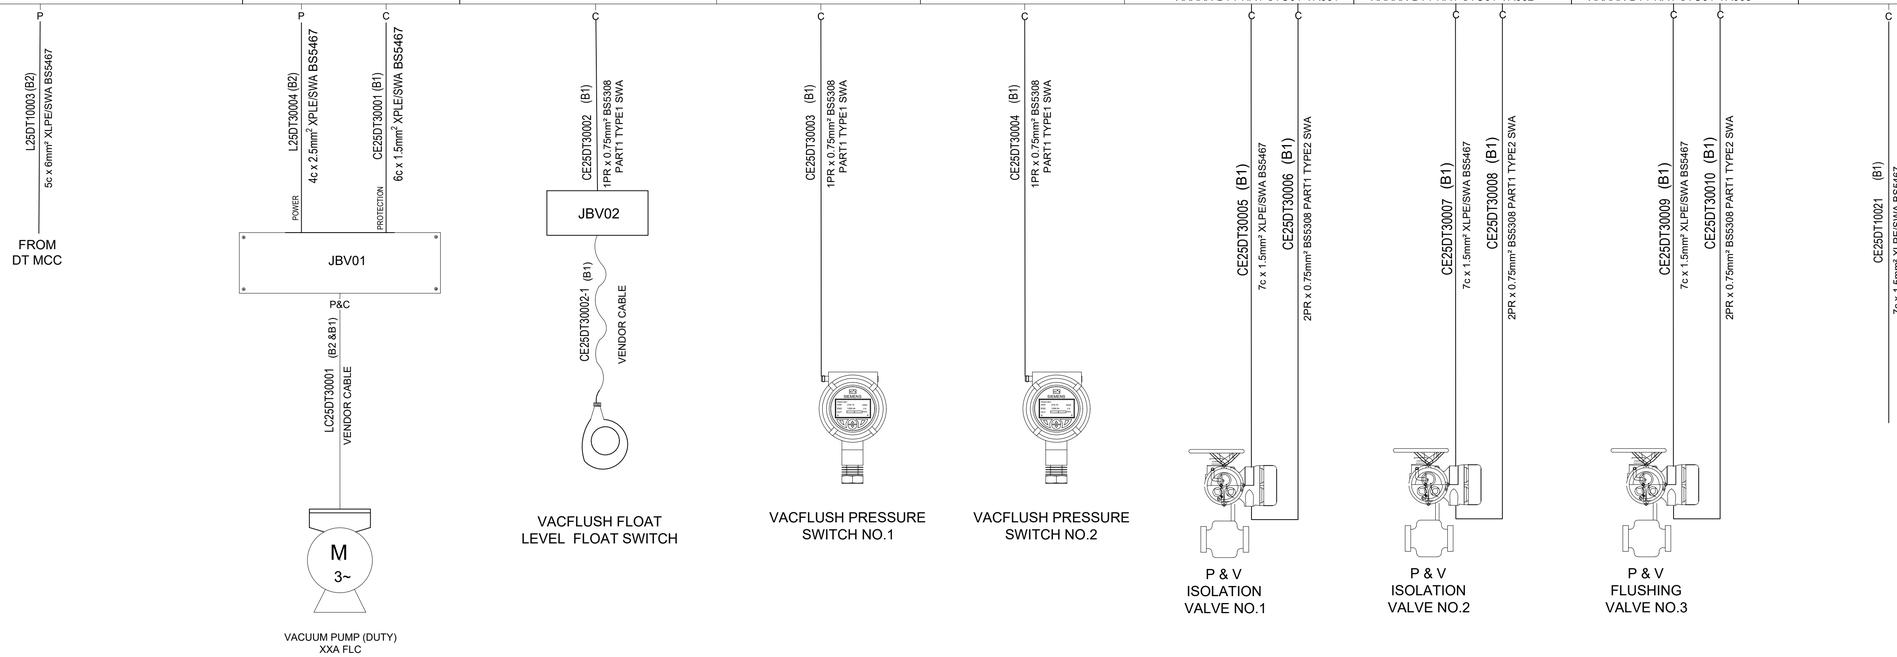

REFERENCE	VALVE ACTUATOR DISTRIBUTION BOARD			
COMPARTMENT				
TYPE/ SIZE	100A ISOLATOR	60898 - S/P - MCB / 6 AMP TYPE B	60898 - S/P - MCB / 6 AMP TYPE B	60898 - S/P - MCB / 6 AMP TYPE B
WB REF				
DESCRIPTION	MAINS SUPPLY	P & V ISOLATION VALVE NO.1	P & V ISOLATION VALVE NO.2	FLUSHING (ACTUATED) VALVE NO.3
WAY		XXXXX-DT1-NA1-STO01-VA001	XXXXX-DT1-NA1-STO01-VA002	XXXXX-DT1-NA1-STO01-VA003

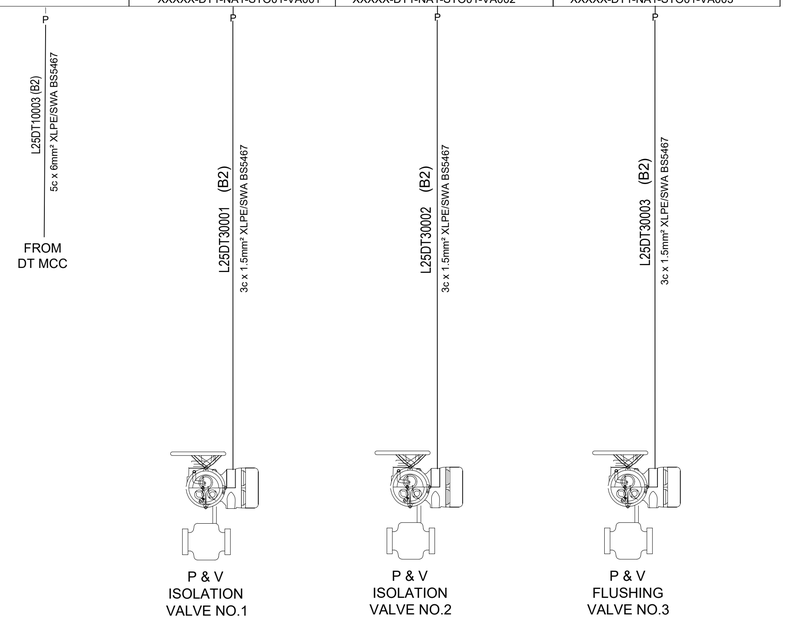

WARD & BURKE

BIM QUALITY SHEET NO:

COPYRIGHT: This drawing is protected by copyright and is not to be reproduced in part or whole form without the prior and written consent of Ward & Burke.

NOTES

1.

REV NO:	DESCRIPTION	DATE	BY
P01	For Information	18/08/25	DG

United Utilities
Water for the North West

PROJECT:
Philips Road

TITLE:
VacFlush system BCD

DRAWN BY:	CHECKED BY:	DATE:
DG	JF	18/08/25

SHEET SIZE:	PROJECT NUMBER:
A1	C809 - PHRDET

W&B DRAWING No:	REV:
PHRDET-WAB-01-XX-DR-W-60102	P01

CLIENT DRAWING No:	SCALE:
80065614-01-WAB-05062-NA-DR-E-00003	NTS

CAD FILE: PHRDET-WAB-01-XX-M2-W-60100-BCD

SUITABILITY CODE:
S2 - Suitable For Information