
REFERENCE								
COMPARTMENT	BUILDING SERVICES DISTRIBUTION BOARD							
TYPE/ SIZE	60898 - S/P - MCB / 16 AMP TYPE B	60898 - S/P - MCB / 6 AMP TYPE B	60898 - S/P - MCB / 6 AMP TYPE C	60898 - S/P - MCB / 6 AMP TYPE C	60898 - S/P - MCB / 10 AMP TYPE C	60898 - S/P - MCB / 6 AMP TYPE B	60898 - S/P - MCB / 6 AMP TYPE B	
WB REF								
DESCRIPTION	SOCKET	HEATER	EXTRACTOR FAN	INTERNAL LIGHTS	DRY WELL LIGHTING	FIRE ALARM	TELEMETRY OUTSTATION	MAINS INCOMER
WAY	WAY 1 L1	WAY 1 L2	WAY 1 L3	WAY 2 L1	WAY 2 L2	WAY 2 L3	WAY 3 L1	

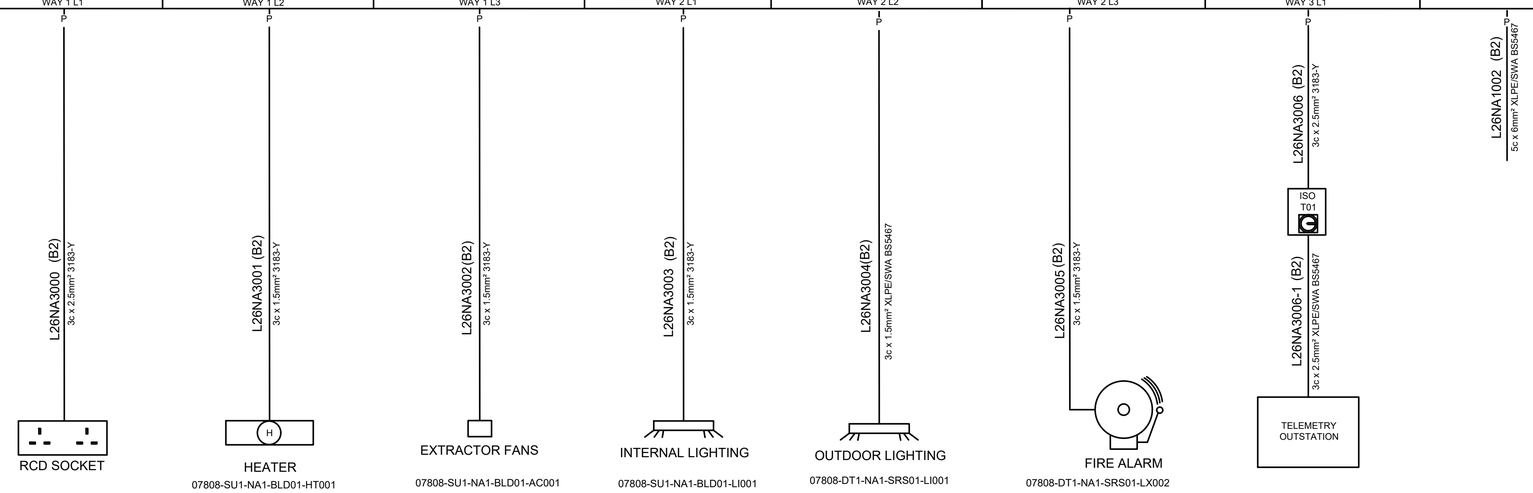

WARD & BURKE

BIM QUALITY SHEET NO:

COPYRIGHT: This drawing is protected by copyright and is not to be reproduced in part or whole form without the prior and written consent of Ward & Burke.

NOTES

REV NO:	DESCRIPTION	DATE	BY
P01	For Information	27/07/26	DG

United Utilities
Water for the North West

PROJECT:
Knutsford WwTW

TITLE:
Building Services BCD

DRAWN BY:	CHECKED BY:	DATE:
AS	DG	21/04/2026

SHEET SIZE:	PROJECT NUMBER:
A1	C783 - KNUTDT

W&B DRAWING No:	REV:
KNUTDT-WAB-03-XX-DR-W-60203	P01

CLIENT DRAWING No:	SCALE:
	NTS

CAD FILE: KNUTDT-WAB-03-XX-M2-W-60200-BCD

SUITABILITY CODE: S01 - For Information