
REFERENCE	MARSHALLING BOX - VALVE PAD							
COMPARTMENT								
TYPE/ SIZE								
WB REF								
DESCRIPTION	STORM TRANSFER PUMP NO.1 FLOWMETER	STORM TRANSFER PUMP NO.2 FLOWMETER	STORM TRANSFER ACTUATED VALVE NO.1	STORM TRANSFER ACTUATED VALVE NO.2	STORM TRANSFER PUMP NO.1 NRV	STORM TRANSFER PUMP NO.2 NRV	STORM TRANSFER PS RADAR LEVEL NO.1	STORM TRANSFER PS RADAR LEVEL NO.2
TAG	KNUTF-NP1-NA1-PMS01-FX001	KNUTF-NP1-NA1-PMS01-FX002	KNUTF-NP1-NA1-PMS01-VA001	KNUTF-NP1-NA1-PMS01-VA002	KNUTF-NP1-NA1-PMS01-PU001	KNUTF-NP1-NA1-PMS01-PU002	KNUTF-NP1-NA1-PMS01-LX001	KNUTF-NP1-NA1-PMS01-LX001

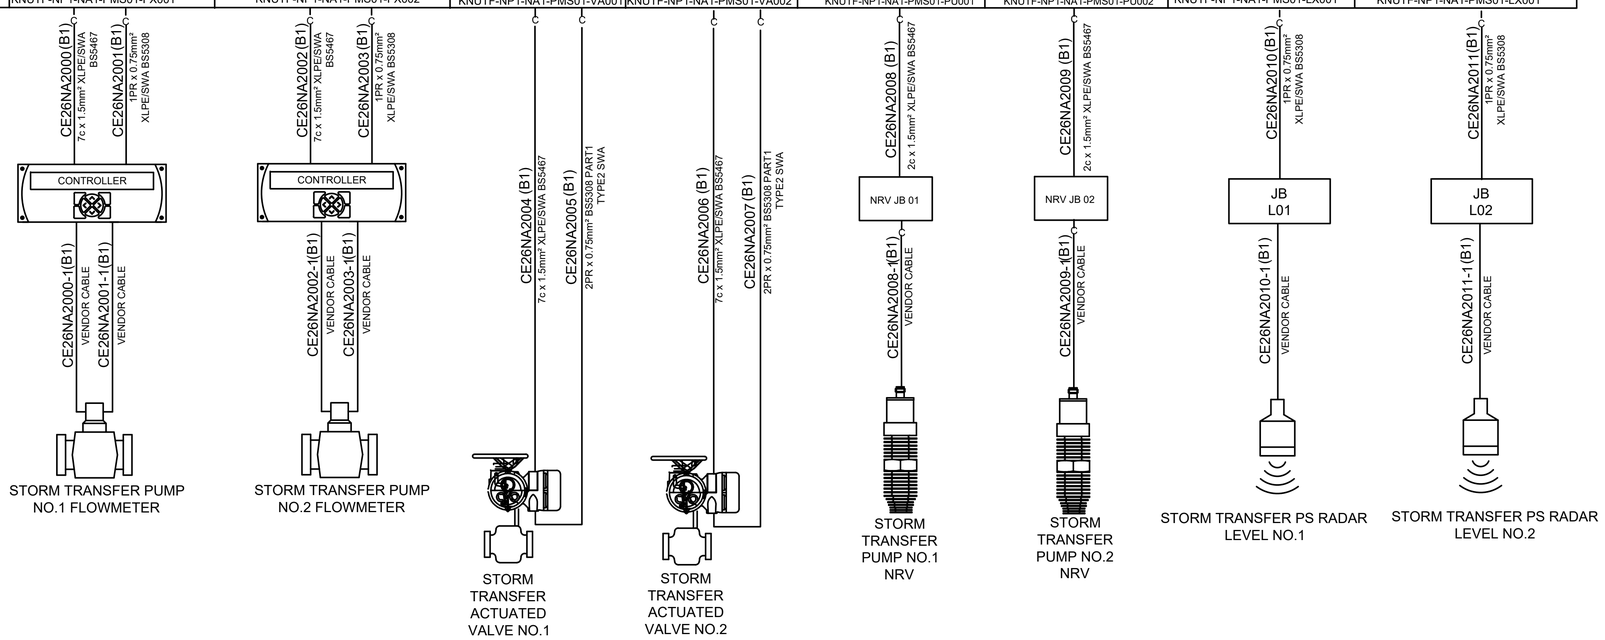

WARD & BURKE

BIM QUALITY SHEET NO:

COPYRIGHT: This drawing is protected by copyright and is not to be reproduced in part or whole form without the prior and written consent of Ward & Burke.

NOTES

REV NO:	DESCRIPTION	DATE	BY
P01	For Information	27/07/26	DG

United Utilities
Water for the North West

PROJECT:
Knutsford WwTW

TITLE:
MARSHALLING BOX

DRAWN BY:	CHECKED BY:	DATE:
AS	DG	21/04/2026

SHEET SIZE:	PROJECT NUMBER:
A1	C783 - KNUSDT

W&B DRAWING No:	REV:
KNUTDT-WAB-03-XX-DR-W-60202	P01

CLIENT DRAWING No:	SCALE:
	NTS

CAD FILE: KNUTDT-WAB-03-XX-M2-W-60200-BCD

SUITABILITY CODE: S01 - For Information