
REFERENCE	BUILDING SERVICES DISTRIBUTION BOARD							
COMPARTMENT								
TYPE/ SIZE	ISOLATOR - 63A	60898 - S/P - MCB / 16 AMP TYPE B	60898 - S/P - MCB / 6 AMP TYPE B	60898 - S/P - MCB / 6 AMP TYPE B	60898 - S/P - MCB / 63 AMP TYPE C	60898 - S/P - MCB / 6 AMP TYPE C	60898 - S/P - MCB / 6 AMP TYPE C	60898 - S/P - MCB / 6 AMP TYPE C
WB REF								
DESCRIPTION	MAINS INCOMER	SOCKET	LIGHTING	HEATER	SPD	SMOKE DETECTOR	SPARE	TELEMETRY OUTSTATION
WAY		WAY 1 L1	WAY 3 L1	WAY 1 L3	WAY 2 L1-L2-L3	WAY 1 L2	WAY 3 L2	WAY 3 L1

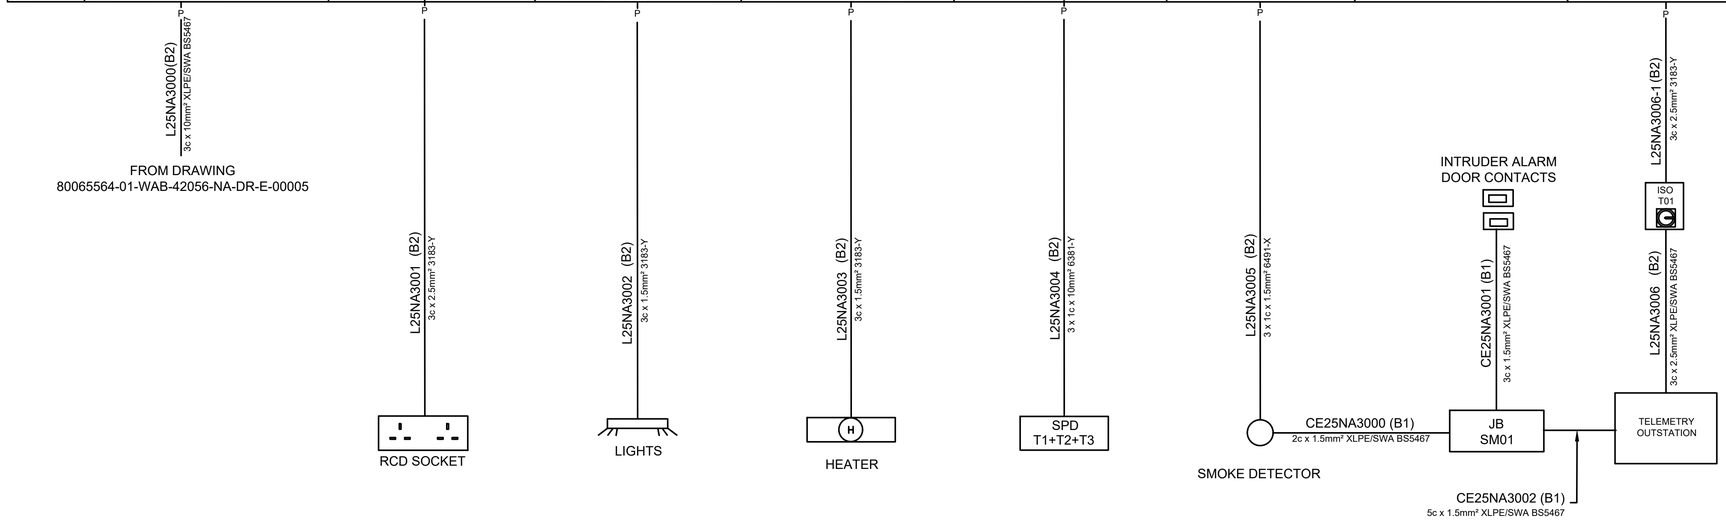

WARD & BURKE

BIM QUALITY SHEET NO:

COPYRIGHT: This drawing is protected by copyright and is not to be reproduced in part or whole form without the prior and written consent of Ward & Burke.

NOTES

REV NO:	DESCRIPTION	DATE	BY
P01	For Information	16/06/25	DG
P02	For Information	11/07/25	DG
C01	For Information	21/04/26	DG

United Utilities
Water for the North West

PROJECT:
Gaskell Street

TITLE:
Building Services BCD

DRAWN BY:	CHECKED BY:	DATE:
AS	DG	21/04/2026

SHEET SIZE:	PROJECT NUMBER:
A1	C821 - GASKST

W&B DRAWING No:	REV:
GASKST-WAB-01-XX-DR-W-60103	C01

CLIENT DRAWING No:	SCALE:
80065564-01-WAB-42056-NA-DR-E-00004	NTS

CAD FILE: GASKST-WAB-01-XX-M2-W-60100-BCD

SUITABILITY CODE:
CR - Construction Record