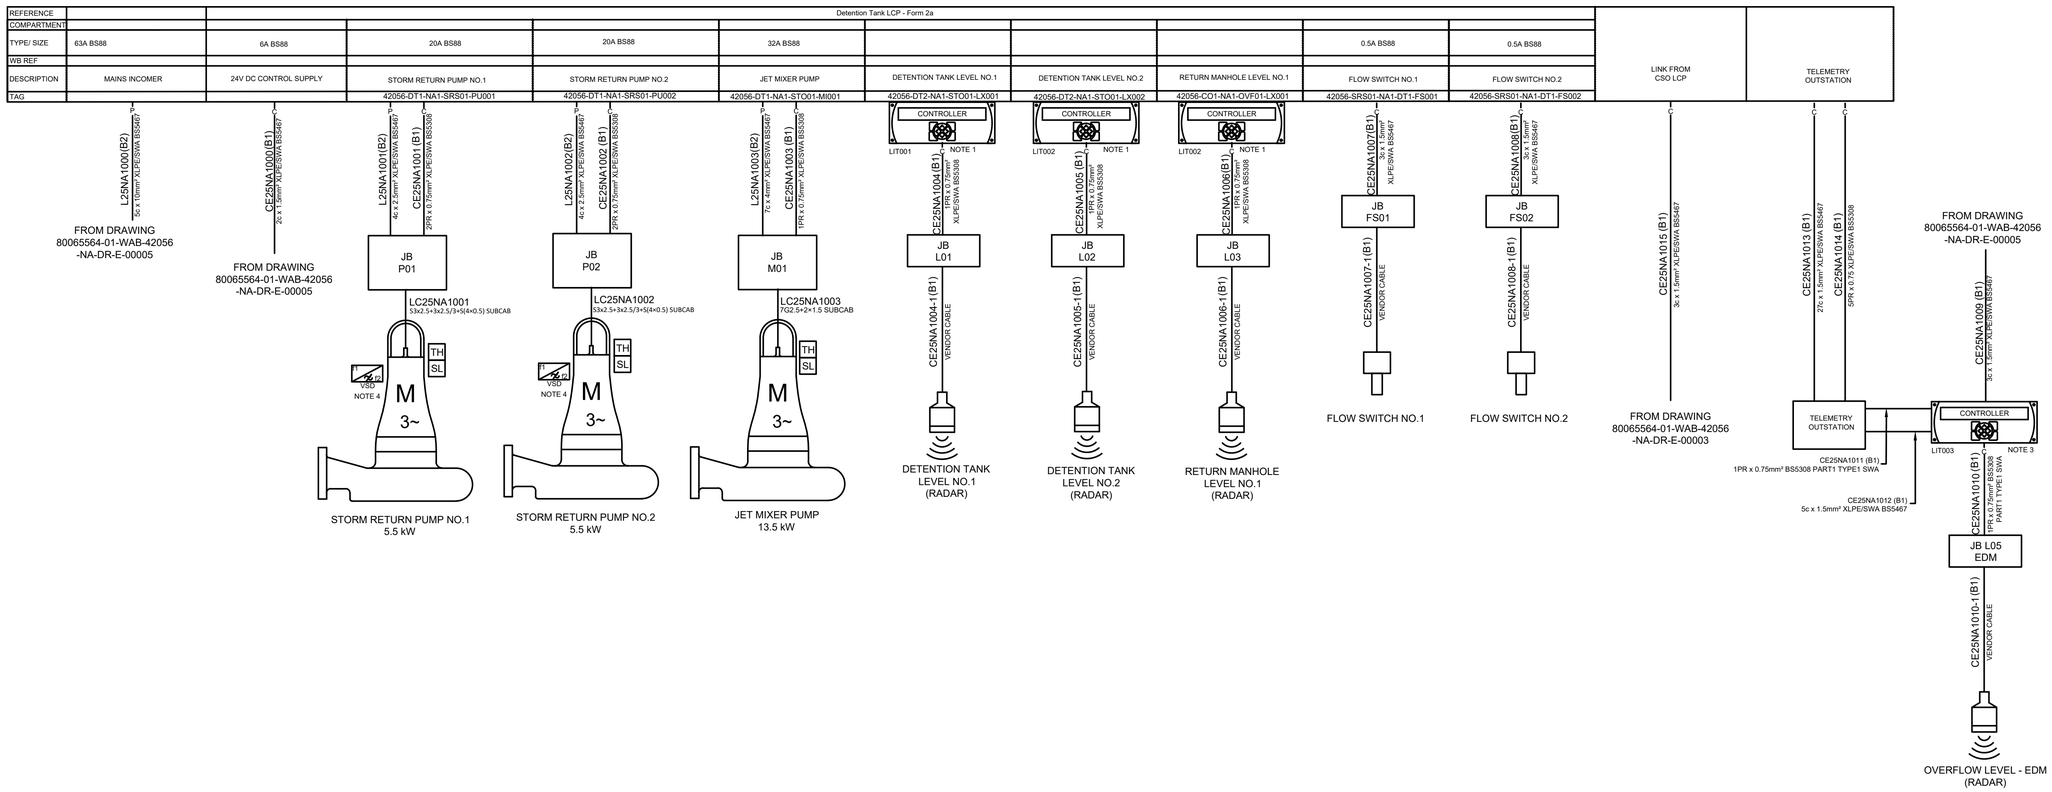


WARD & BURKE

BIM QUALITY SHEET NO:

COPYRIGHT: This drawing is protected by copyright and is not to be reproduced in part or whole form without the prior and written consent of Ward & Burke.

NOTES

1. LEVEL CONTROLLERS MOUNTED ON PANEL DOORS
2. INSOLATOR ISOLATION PROVIDES ISOLATION FROM THE LCP SOURCE TO ENSURE ISOLATOR IS DEAD ON THE SUPPLY SIDE WHEN ENCLOSURE IS OPEN
3. WALL-MOUNTED LEVEL CONTROLLER
4. VSD INCLUDED IN PUMP HOUSING

REV NO:	DESCRIPTION	DATE	BY
P01	For Information	16/06/25	DG
P02	For Information	11/07/25	DG
C01	For Information	21/04/26	AS

United Utilities
Water for the North West

PROJECT:

Gaskell Street

TITLE:

DT BCD

DRAWN BY:	CHECKED BY:	DATE:
AS	DG	21/04/2026

SHEET SIZE:	PROJECT NUMBER:
A1	C821 - GASKST

W&B DRAWING No:	REV:
GASKST-WAB-01-XX-DR-W-60101	C01

CLIENT DRAWING No:	SCALE:
80065564-01-WAB-42056-NA-DR-E-00002	NTS

CAD FILE: GASKST-WAB-01-XX-M2-W-60100-BCD

SUITABILITY CODE: CR - Construction Record